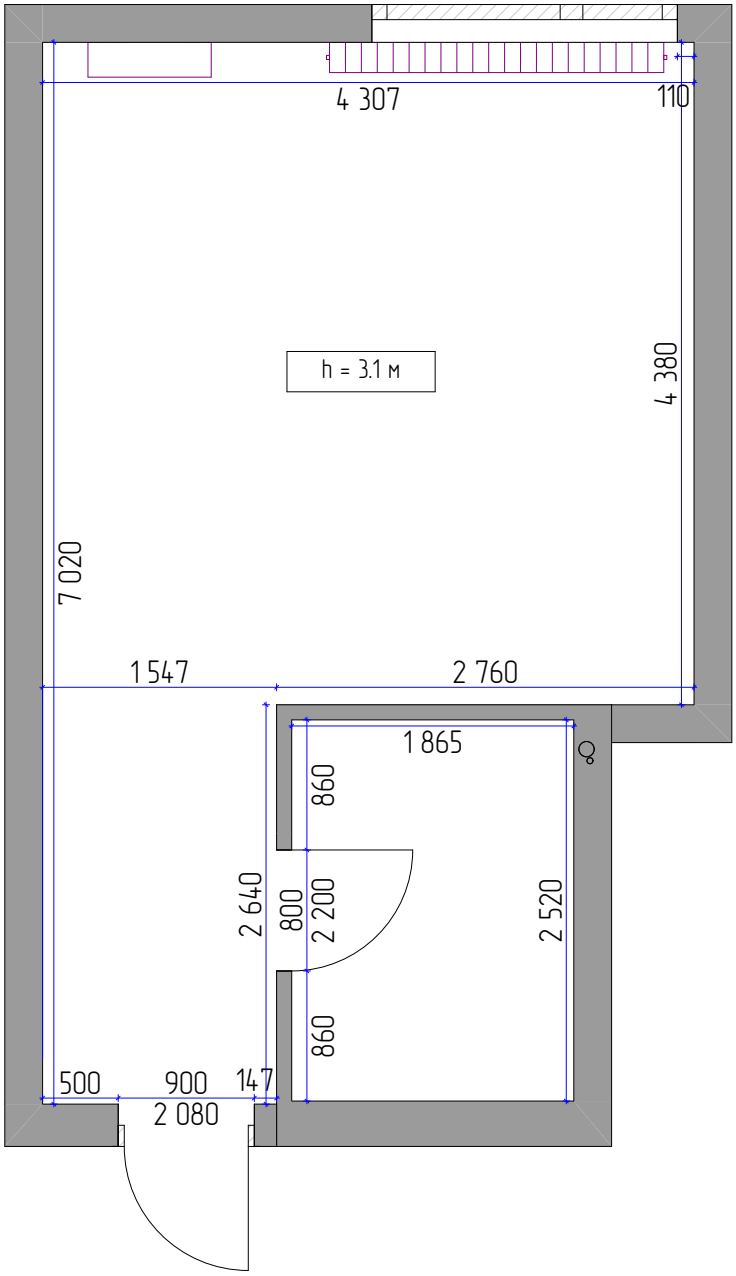


## Условные обозначения:

– Стены

500 – Размер в мм

## Примечание:

1. Все замеры произведены от черновых (неоштукатуренных) поверхностей стен и перегородок.
2. Приведенные размеры являются фактическими на момент фиксации. После выравнивания стен, штукатурных и отделочных работ (шпаклевка, плитка, стеновые панели) габариты помещений уменьшатся. Расчетная толщина слоя штукатурки и отделки в данном проекте условно принята за 20–30 мм на каждую стену.
3. Все критически важные размеры (для встроенной мебели, кухонных гарнитуров, инсталляций, дверных проемов и сантехнического оборудования) необходимо повторно проверить и уточнить по месту после завершения этапа оштукатуривания и выравнивания стен.
4. Все выводы инженерных сетей (водопровод, канализация, вентиляция, электрика) привязаны к черновым стенам. Строительной бригаде необходимо учесть толщину будущего финишного слоя при монтаже оконечных устройств и сантехники.
5. В ходе демонтажных или подготовительных работ параметры помещений (высоты, углы, геометрия) могут измениться. При обнаружении значительных расхождений с данным планом (более 15–20 мм) необходимо незамедлительно уведомить автора проекта для внесения корректировок.

| | | |
|---|---|---|
| Масштаб 1:50 | Москва студия 27.8 м. кв. | |
| | Обмерный план | Лист |
| | | 3 |
| | | Дата |
| | | 15.10.26 |